




CLIENT: NATIONAL HIGHWAYS AUTHORITY OF INDIA		PROJECT: CONSTRUCTION OF INTEGRATED STRUCTURES ALONG WITH DEVELOPMENT OF OTHER ALLIED STRUCTURES ON BOTH SIDES OF CHANDANI CHOK JUNCTION (KM. 942.980) OF NH-4 IN PUNE CITY IN THE STATE OF MAHARASHTRA ON EPC MODE	
CONSULTANT: XCC ENGINEERS AND PLANNERS 101, KRISHNA KUNJ, S. V. ROAD, DHBURG (E), MUMBAI - 400 068		TITLE: ROAD LAYOUT PLAN AT Km 942.000 TO 943.600	
DRG. NO. XCC/282/CO/PLAN/801		PAC	
XCC - TEAM LEADER		SCALE: 1:1000	
DATE		DATE	
R.1		R.2	
MODIFIED TO INCLUDE SAFETY ENHANCEMENT FEATURES BY ROAD SAFETY EXPERT TEAM OF NHAI		REVISD AS PER MEETING WITH ROAD SAFETY EXPERT TEAM ON 22/07/2017 (IMPROVEMENT AT VUEP AND PASHAN JUNCTION ABOUT 8' INTRODUCTION OF CHANNELIZATION)	
R.2		R.3	
REVISD AS PER COMMENTS OF MEETING DTD 12/06/2017 WITH IITB		R.4	
DATE		DATE	
MO		MO	